


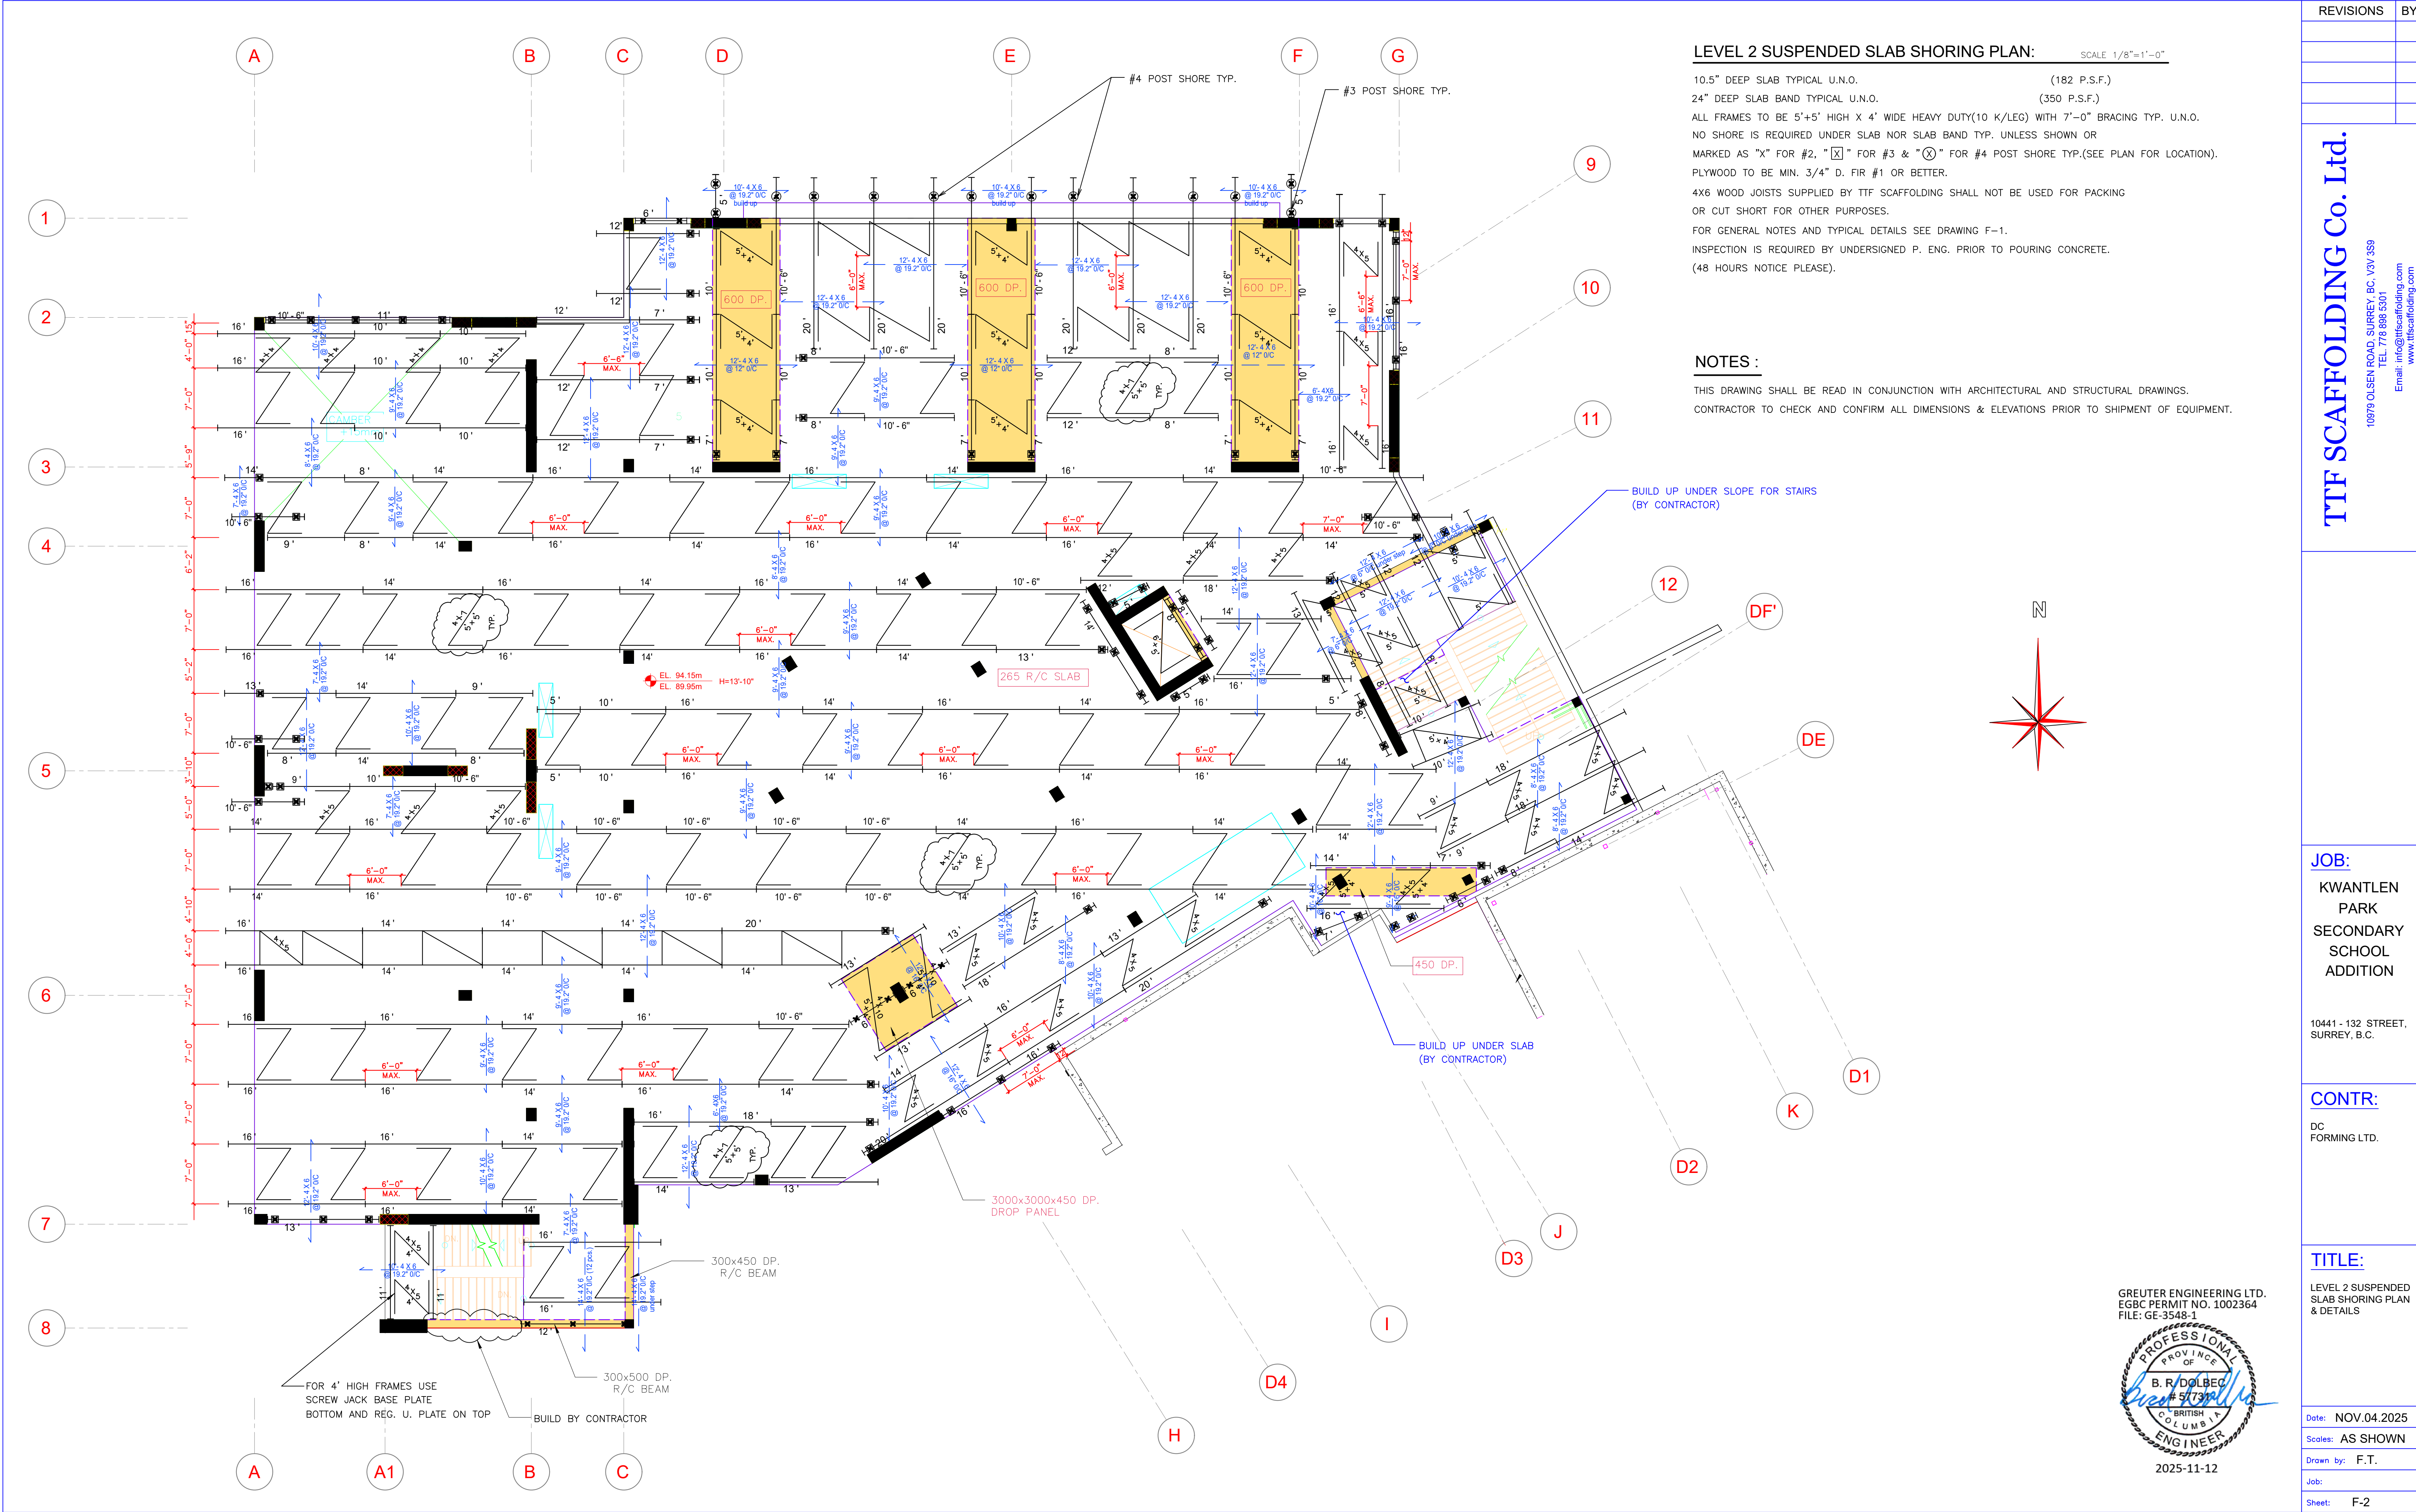

REVISIONS	BY
TTF SCAFFOLDING Co. Ltd.	
10979 OLSEN ROAD, SURREY, BC, V3V 3S9 TEL: 778 888 5301 Email: info@tffscaffolding.com www.tffscaffolding.com	
JOB: KWANTLEN PARK SECONDARY SCHOOL ADDITION	
10441 - 132 STREET, SURREY, B.C.	
CONTR: DC FORMING LTD.	
TITLE: LEVEL 2 SUSPENDED SLAB SHORING PLAN & DETAILS	
Date: NOV.04.2025	
Scales: AS SHOWN	
Drawn by: F.T.	
Job:	
Sheet: F-2	